


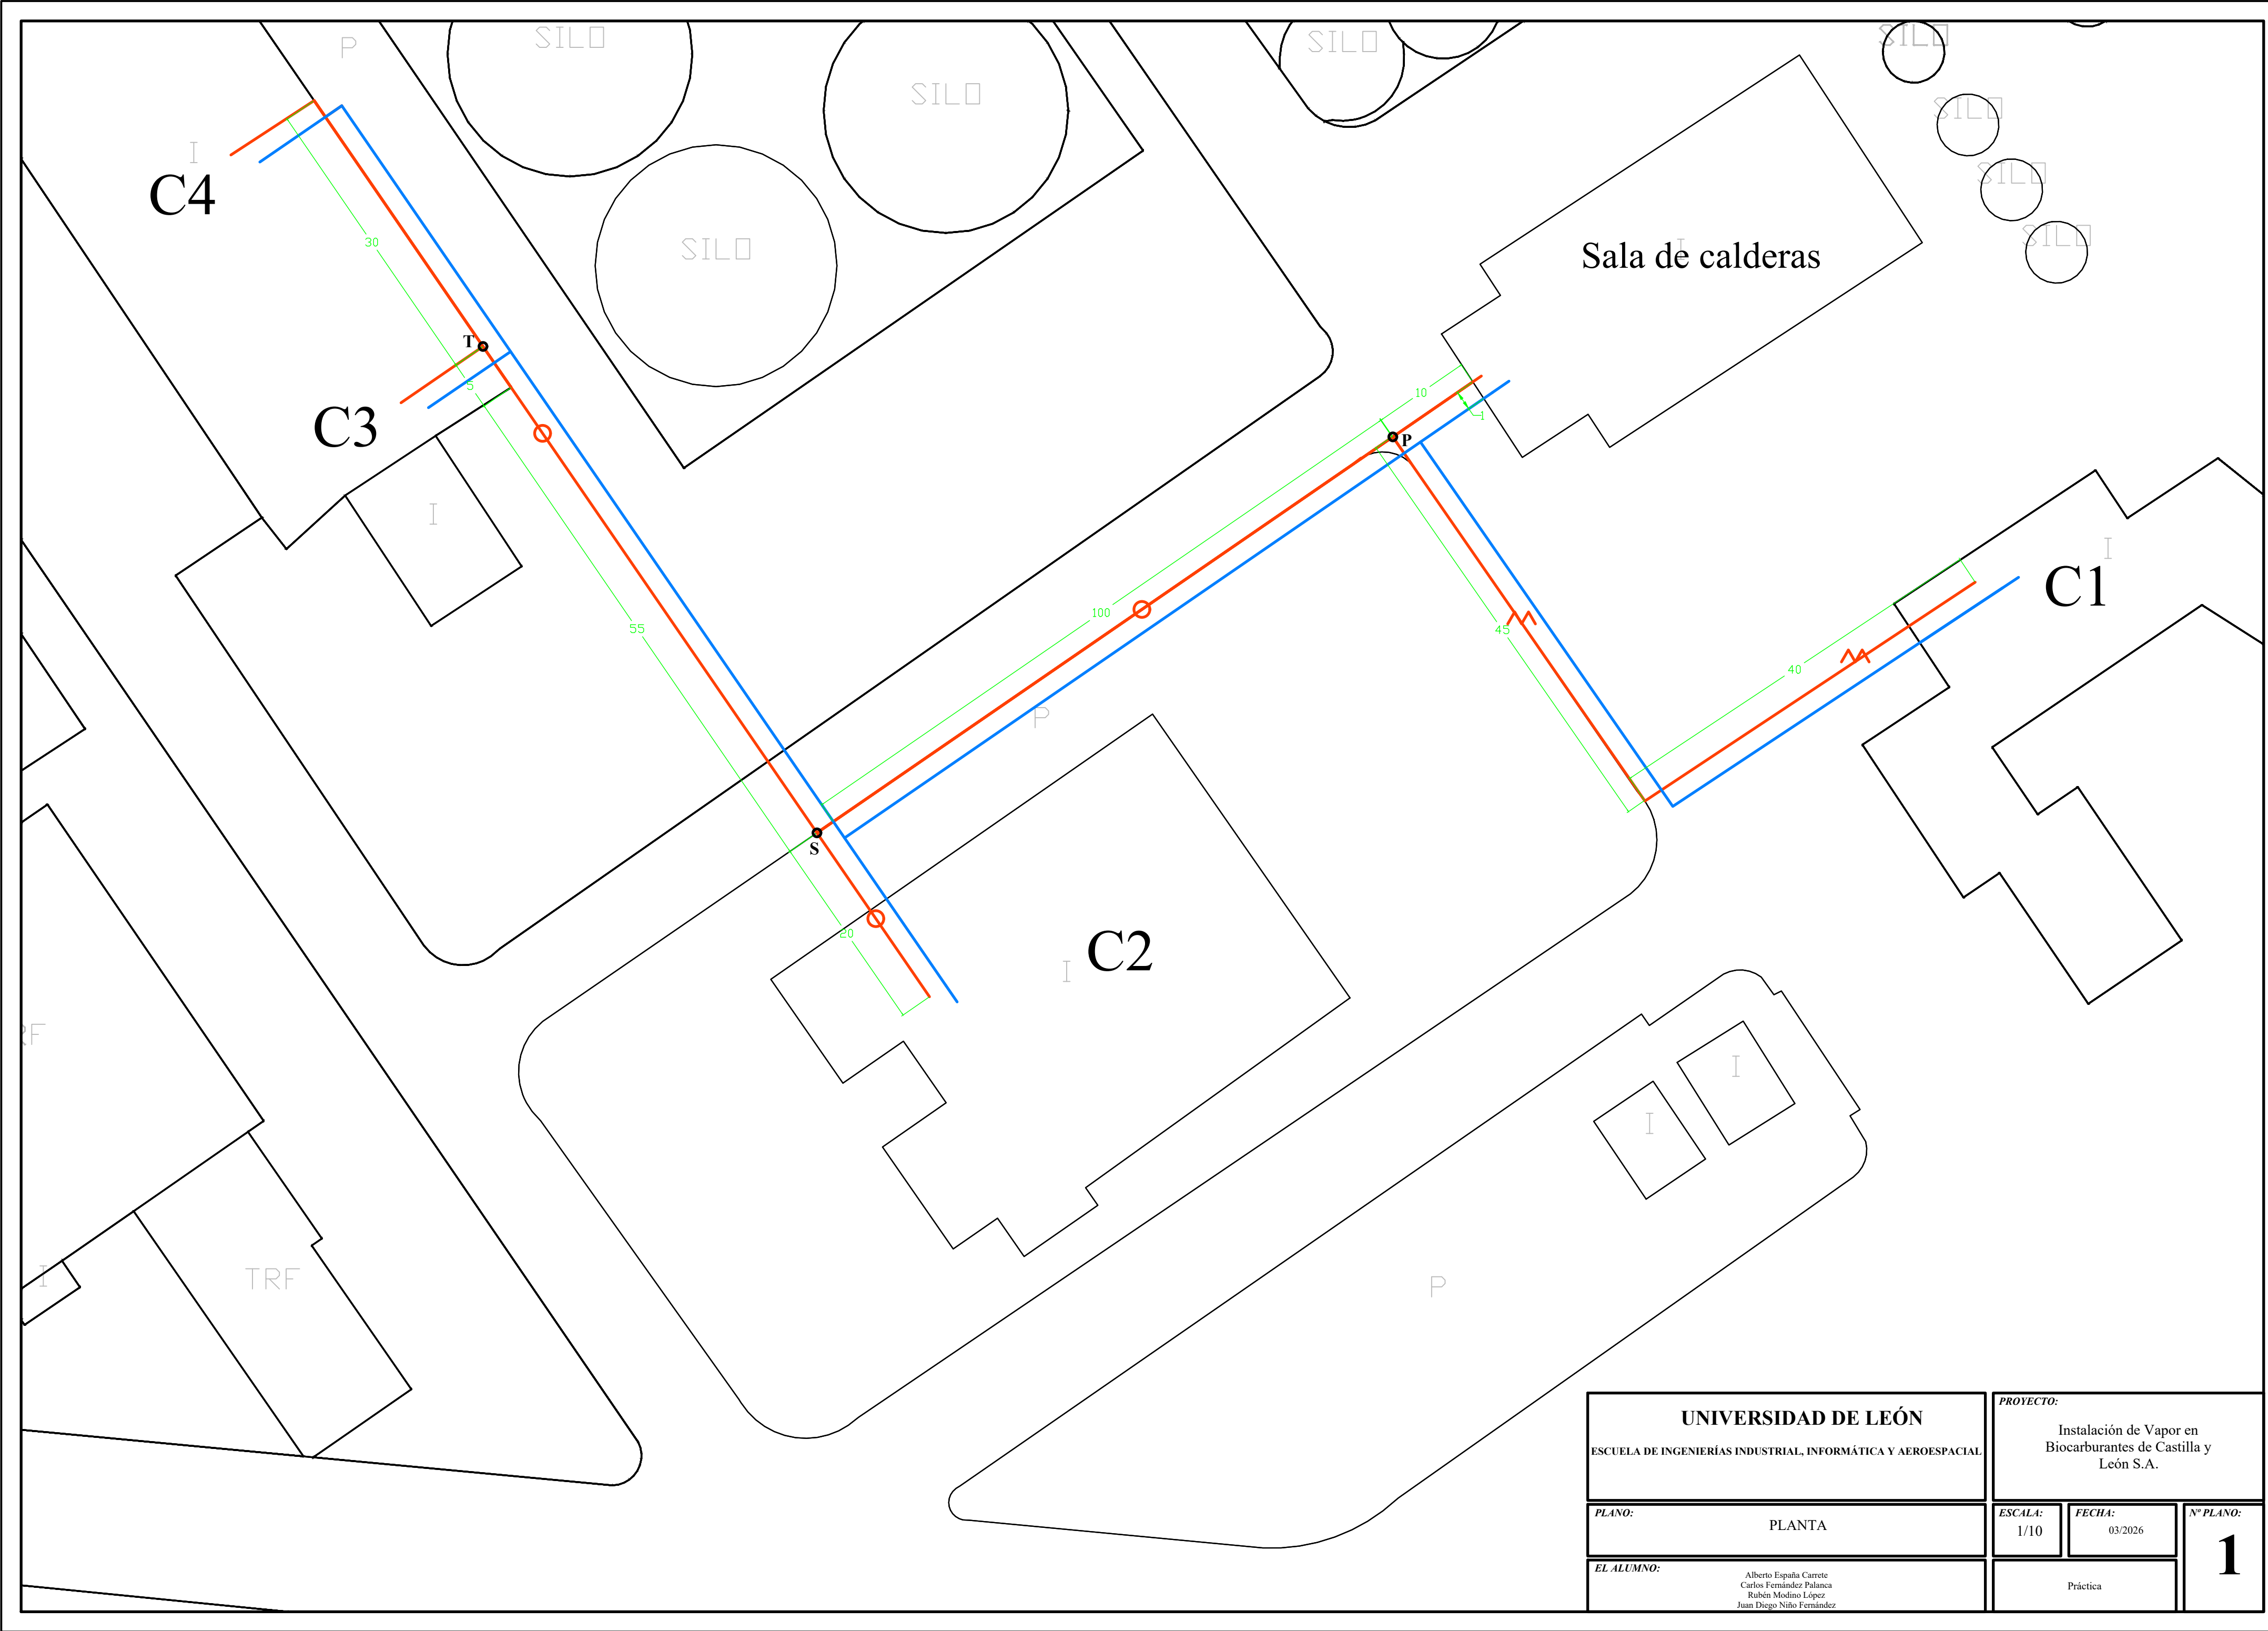

UNIVERSIDAD DE LEÓN ESCUELA DE INGENIERÍAS INDUSTRIAL, INFORMÁTICA Y AEROSPAECIAL		PROYECTO: Instalación de Vapor en Biocarburantes de Castilla y León S.A.	
PLANO:	PLANTA	ESCALA: 1/10	FECHA: 03/2026
EL ALUMNO: Alberto España Carrete Carlos Fernández Palanca Rubén Modino López Juan Diego Niño Fernández		Práctica	Nº PLANO: 1